



NOVO TRAZADO PERIMETRAL,
RECUPERACION DE CAMINO XA EXISTENTE,
CUALIFICACION PARA TRÁFICO RODADO
LIXEIRO PARA CARGA Y DESCARGA E COMO
PASEO PEONIL DE BORDE.

DOTACION DE MOBILIARIO URBANO
NECESARIO . CONSTRUCCION CON
PAVIMENTO DE PEZAS PREFABRICADAS DE
FORMIGÓN CON CRECEMENTO DE
VEXETACIÓN.

AREA DE APARCAMIENTO DESCUBERTO
TRABALLOS DE URBANIZACION.
ADAPTACIÓN A TOPOGRAFIA.




AREA DE APARCAMIENTO DESCUBERTO
TRABALLOS DE URBANIZACION E CONEXION
A NOVOS VIAS.
ADAPTACIÓN A TOPOGRAFIA
PREVISIÓN DE CONEXIONS CON TREASEIRAS
DE VIVENIDAS.



NOVO TRAZADO PERIMETRAL,
RECUPERACION DE CAMINO XA EXISTENTE,
CUALIFICACION PARA TRÁFICO RODADO
LIXEIRO PARA CARGA Y DESCARGA E COMO
PASEO PEONIL DE BORDE.

DOTACION DE MOBILIARIO URBANO
NECESARIO . CONSTRUCCION CON
PAVIMENTO DE PEZAS PREFABRICADAS DE
FORMIGÓN CON CRECEMENTO DE
VEXETACIÓN.

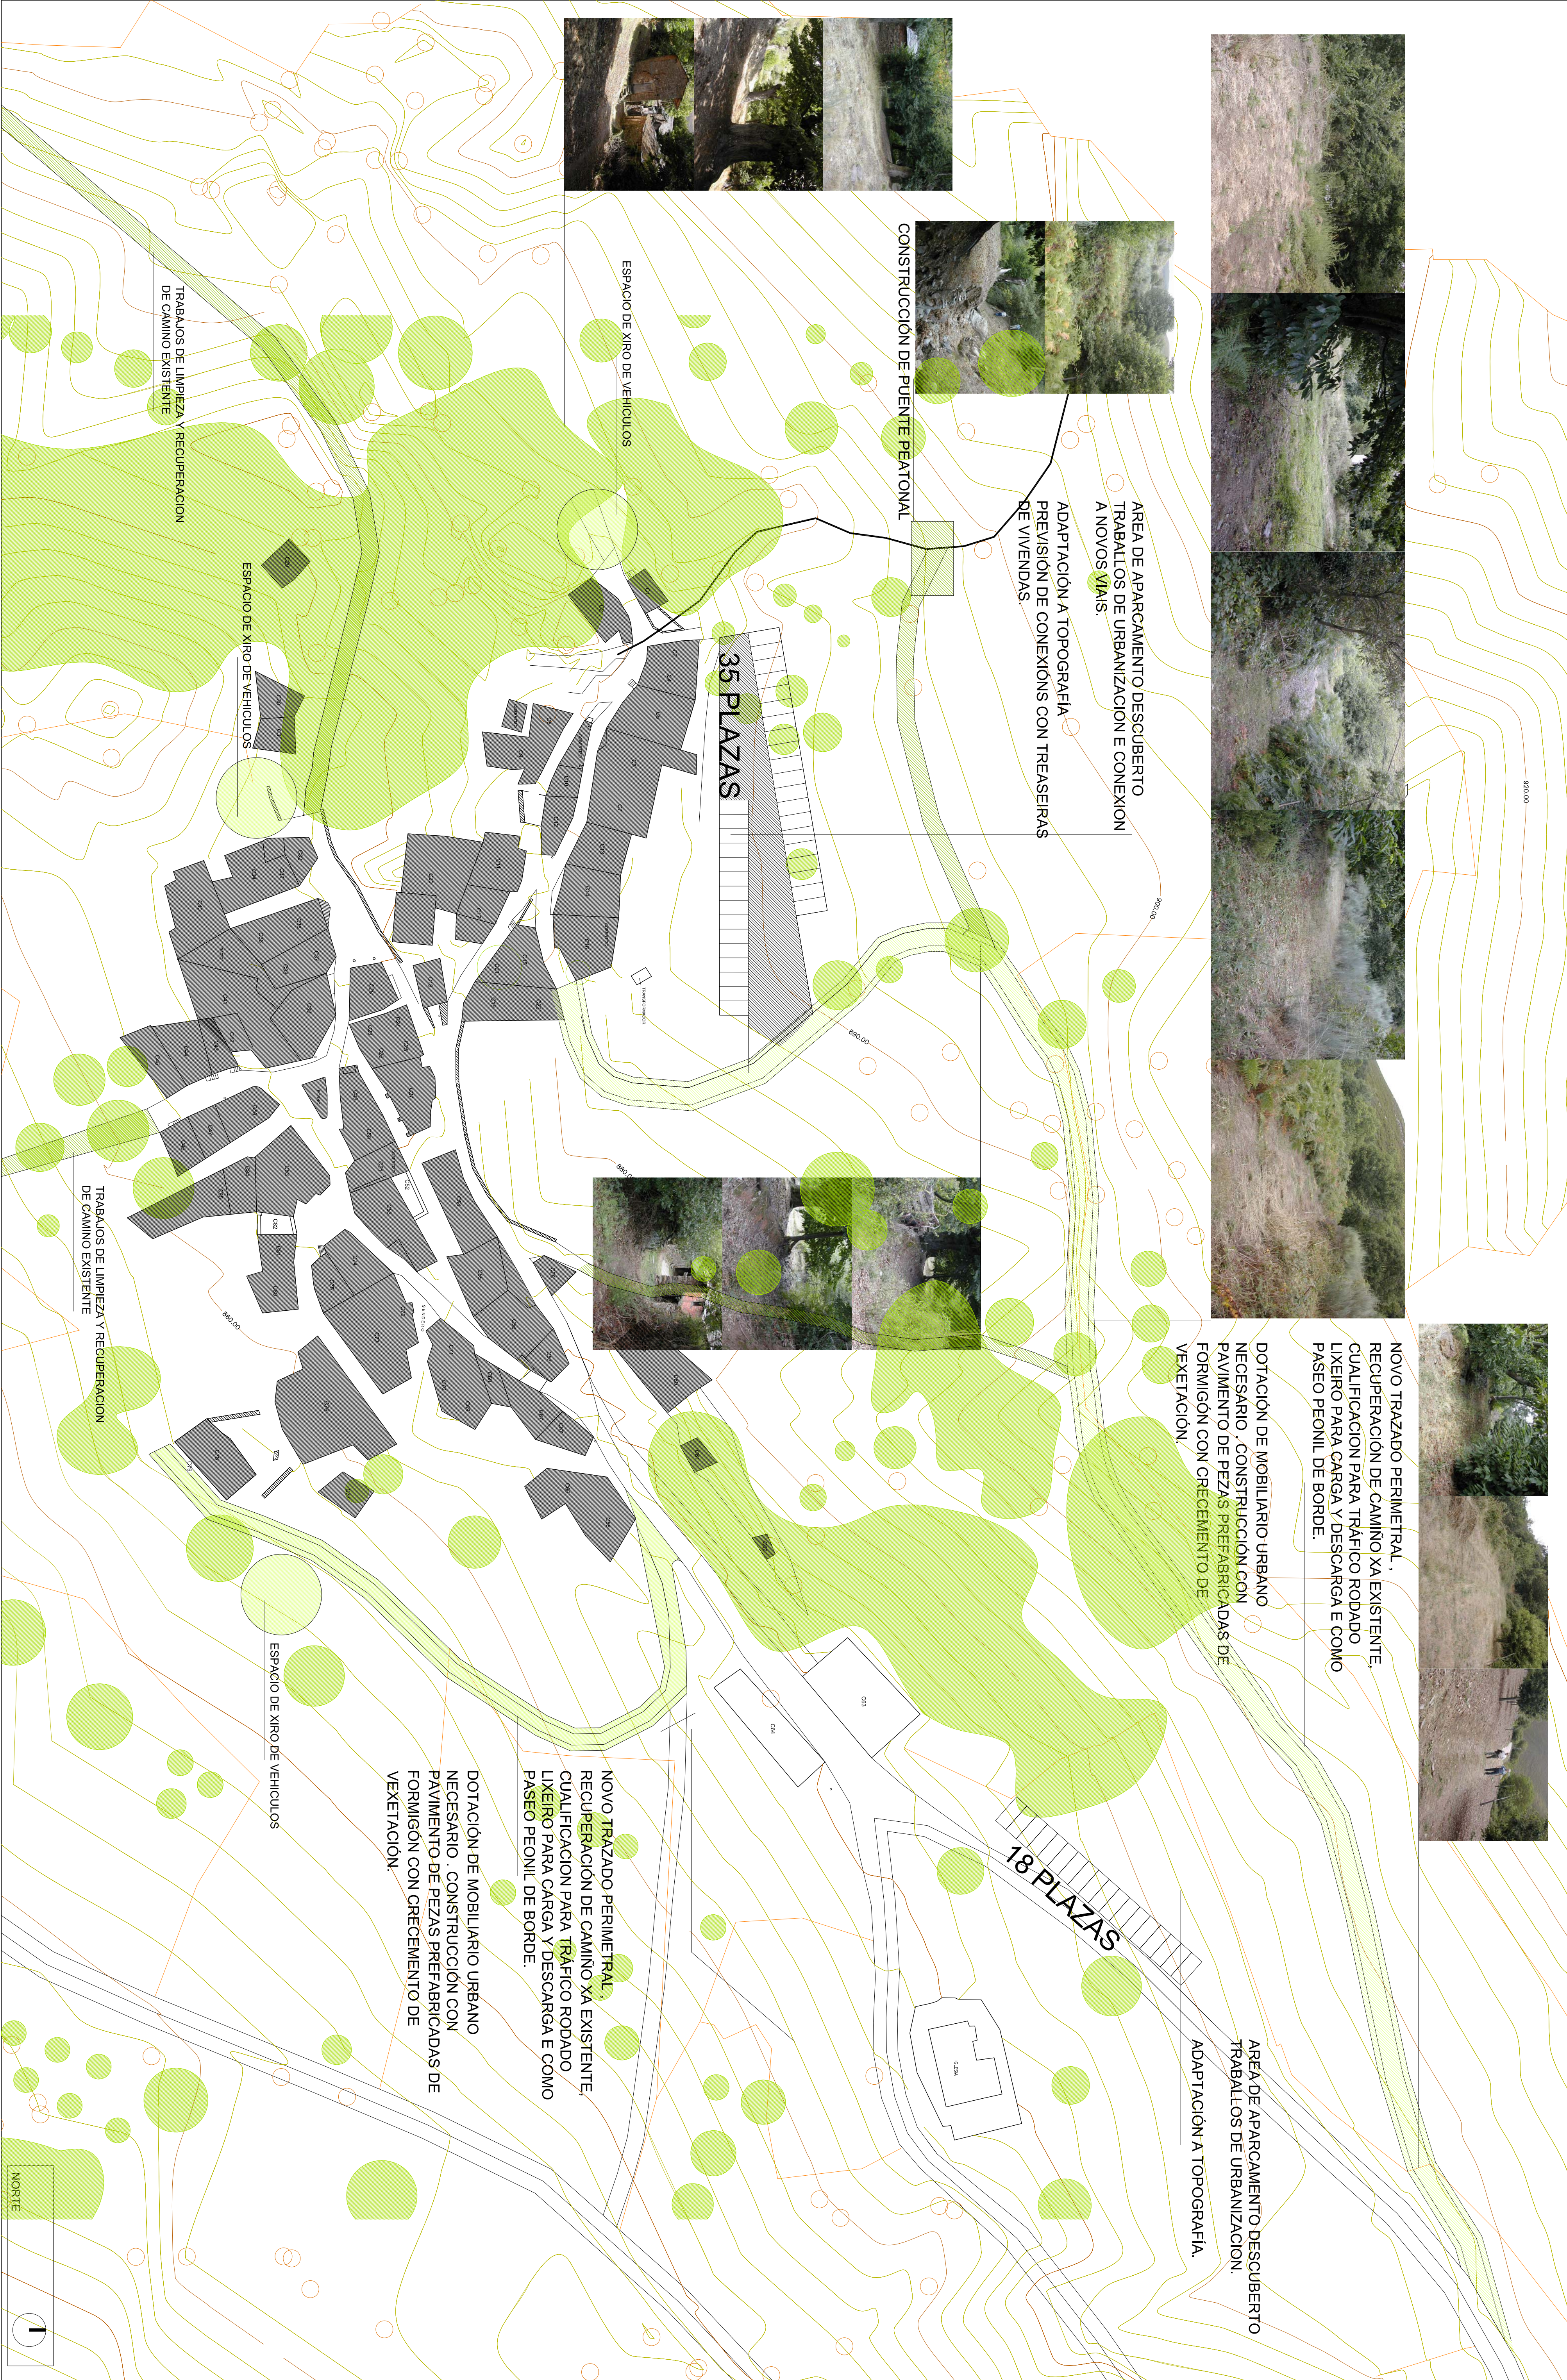

CREACION DE NOVO VIAL PERIMETRAL, RODEANDO O NÚCLEO POLA ZONA NORTE.
VIAL DE TRÁFICO LIXEIRO RESTRIÑIDO. USO PEONIL. COLOCACIÓN DE BANCOS. URBANIZACIÓN ESPACIO PÚBLICO EN TORNO A USOS DE SERVICIOS.
PAVIMENTO PREFABRICADO. FORMIGÓN E VEXETAL.
RESPECTARSE OS CAMINOS EXISTENTES E A VEXETACIÓN.
CONSTRUCCION DE PONTE SOBRE CURSO DE REGATO EXISTENTE.
VIA DE FACIL. EXECUCION. POR TRAZADO EXISTENTE E PROPIEDAD.

VIAL PERIMETRAL DE TRÁFICO RODADO
VIA DE BAIXA CAPACIDADE



PLAN DIRECTOR DE REHABILITACION
ROMADO E CONTORNA
ENCOMENDADO: ASOCIACION DE VECINOS SOCIOCULTURAL
STO. TOME DE ROMADO, A VEIGA, OURENSE
EMPRESARIO: ROMADO-VEIGA-OURENSE

PROPOSTA DE VIAS
A 06
MARZO 2019
ÁREAS DE APARCAMIENTO 1:400