

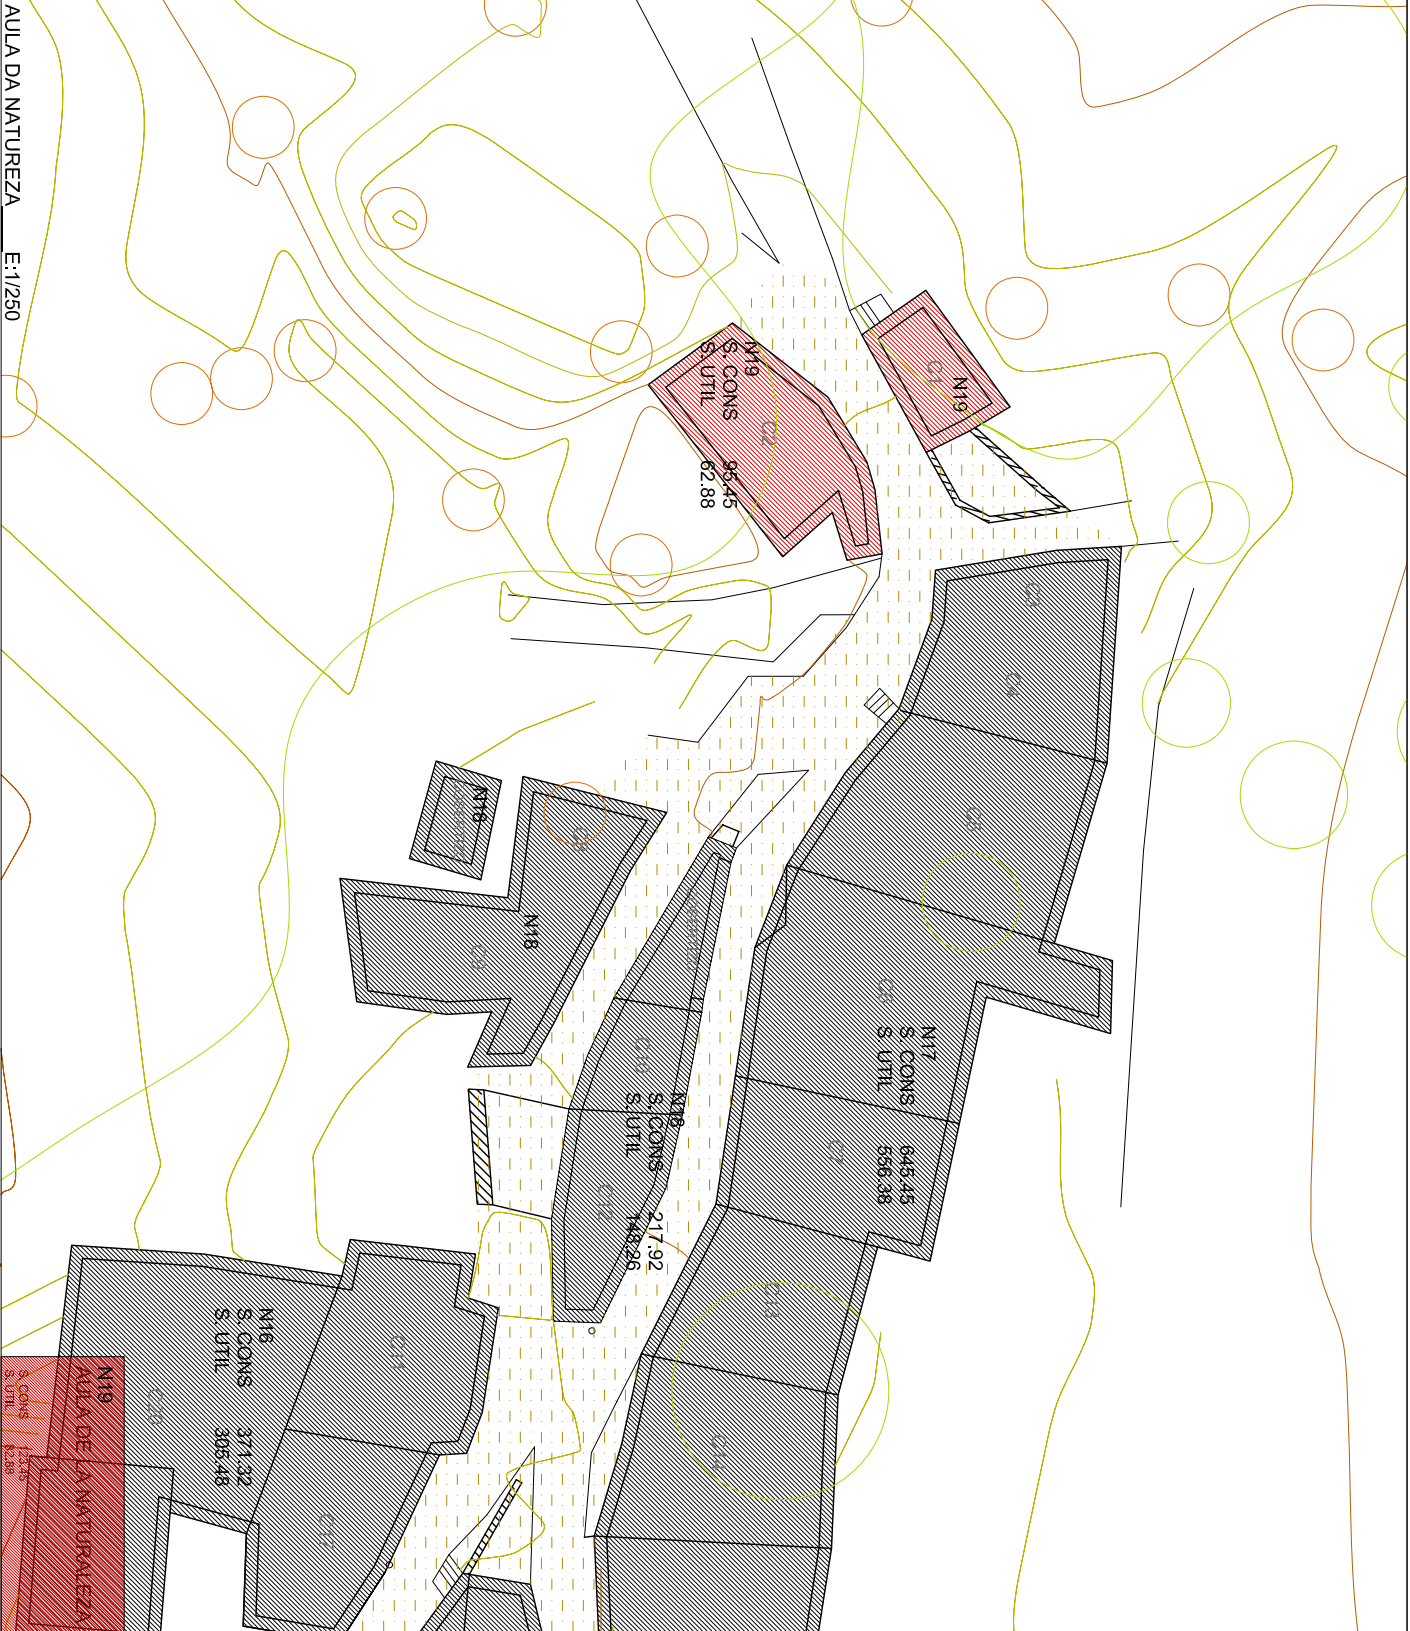
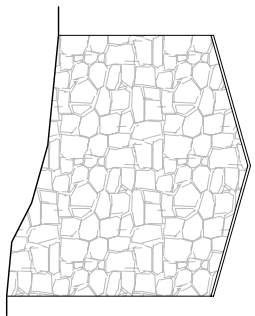
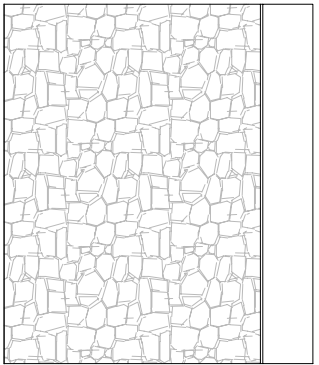
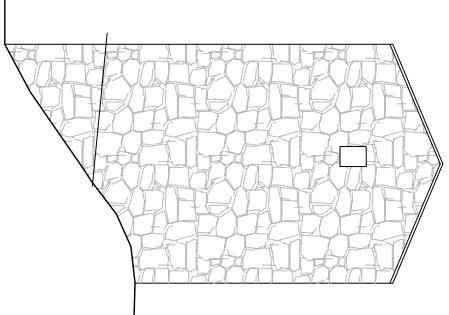
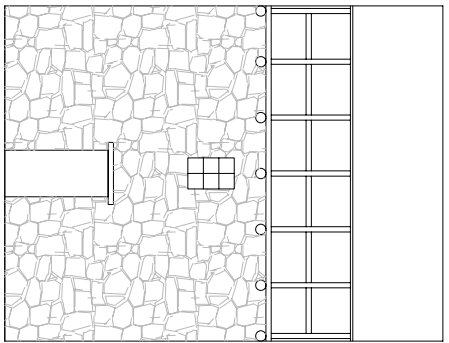
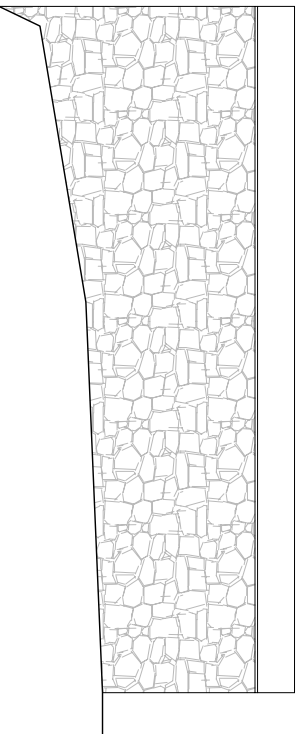


ALZADOS C1 _E:1/100

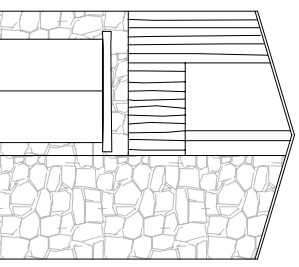


ALZADOS C2 _E:1/100

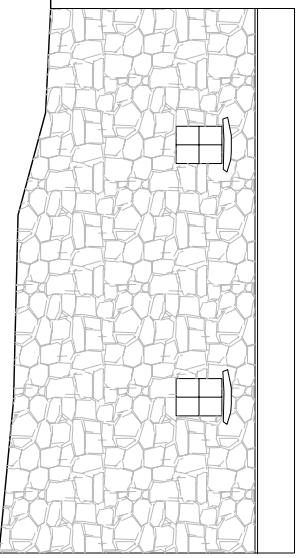

- PROPOSTA DE PROGRAMA: AULA DA NATUREZA
- HALL
 - PEQUENO ESPACIO EXPOSITIVO
 - TALLERES DE TRABAJO
 - ARCHIVO DE MOSTRAS DE CAMPO
 - PEQUENA BIBLIOTECA E SALA DE LECTURA DA NATUREZA
 - DESPACHOS
 - ASEOS
 - ALMACENS


PRESUPUESTO	
S. CONS	123.45
PREP. CONTRATA x m2	996euros
TOTAL	122956.20euros

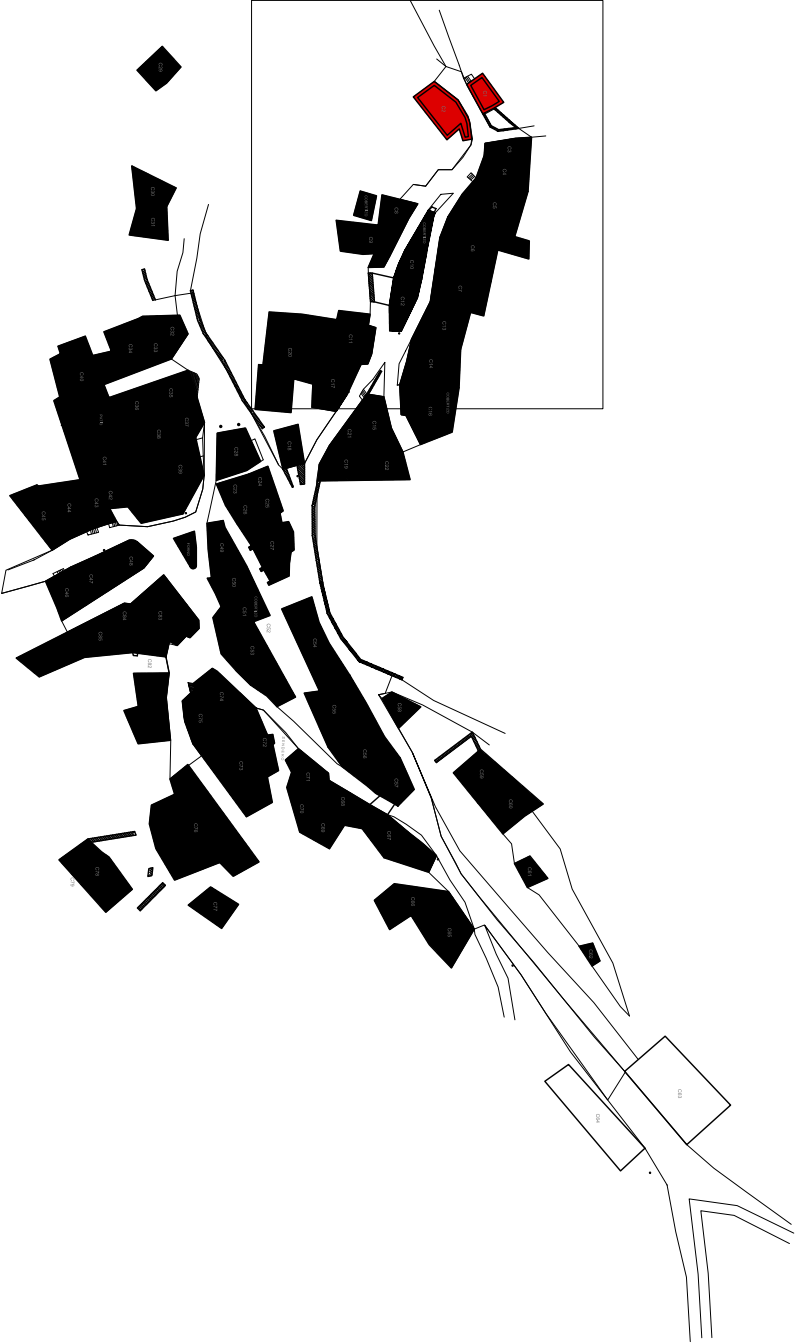

PLANO DE SITUACIÓN E:1/1000



NORTE

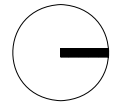

PLAN DIRECTOR DE REHABILITACION
PROBIO E CONSERVACION
enclaucho: SOCIEDADE DE REHABILITACION SOCIOECONOMICA
STO. VOMER DE REHABILITACION A VELHA VELHA
empresamento: romosa veiga-quense

AULA DA NATUREZA
E PAISAXE MONTANESA
plano
A 11
MAY - 2009
SITUACION USOS 1:250